


B-4 Shema kruga električnog prozora

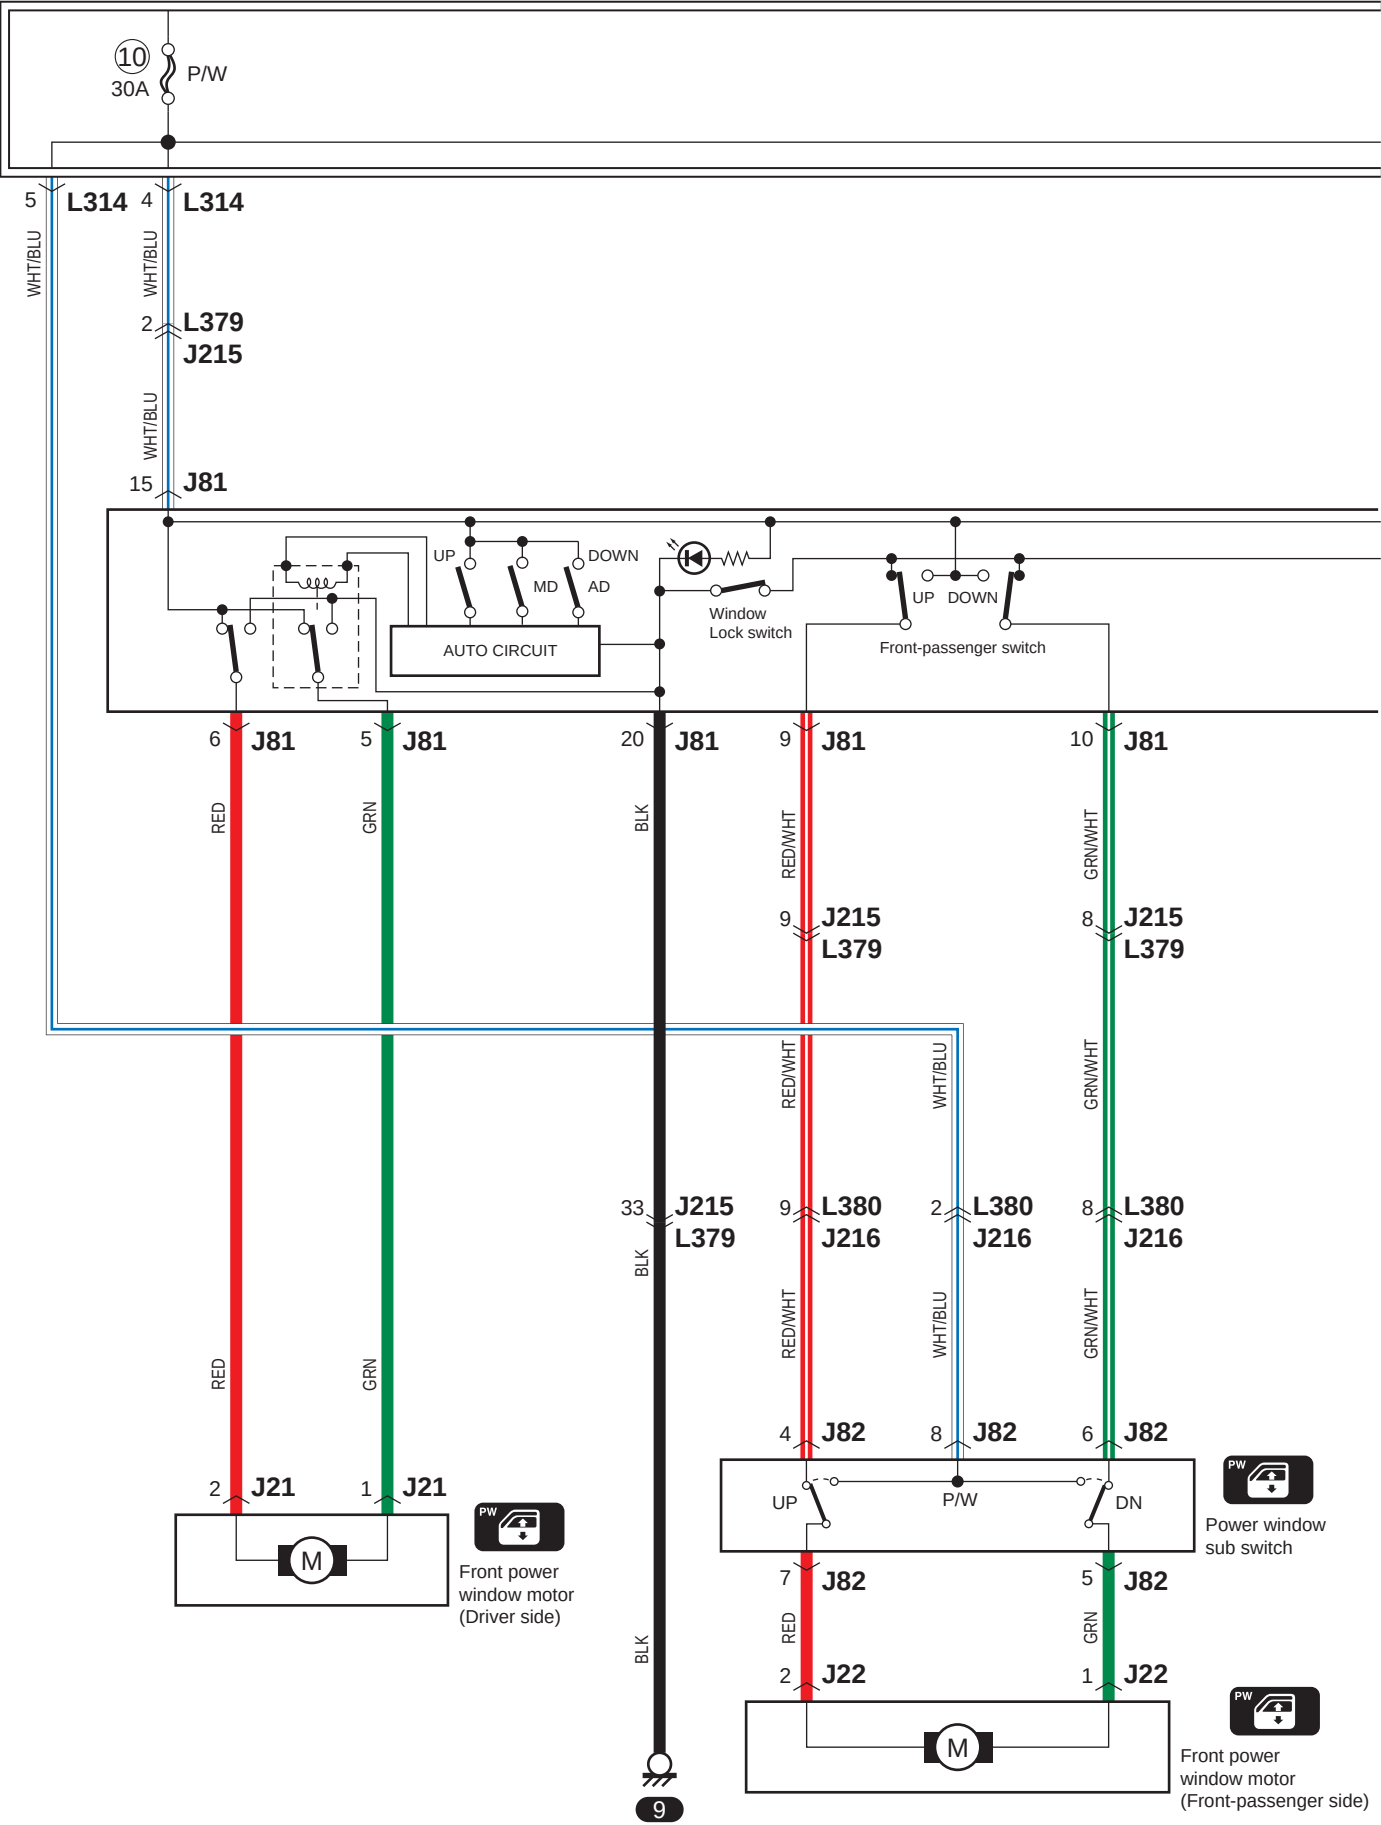

B-4 Shema kruga električnog prozora

