


B-1 Ablaktörő és ablakmosó kapcsolási rajza

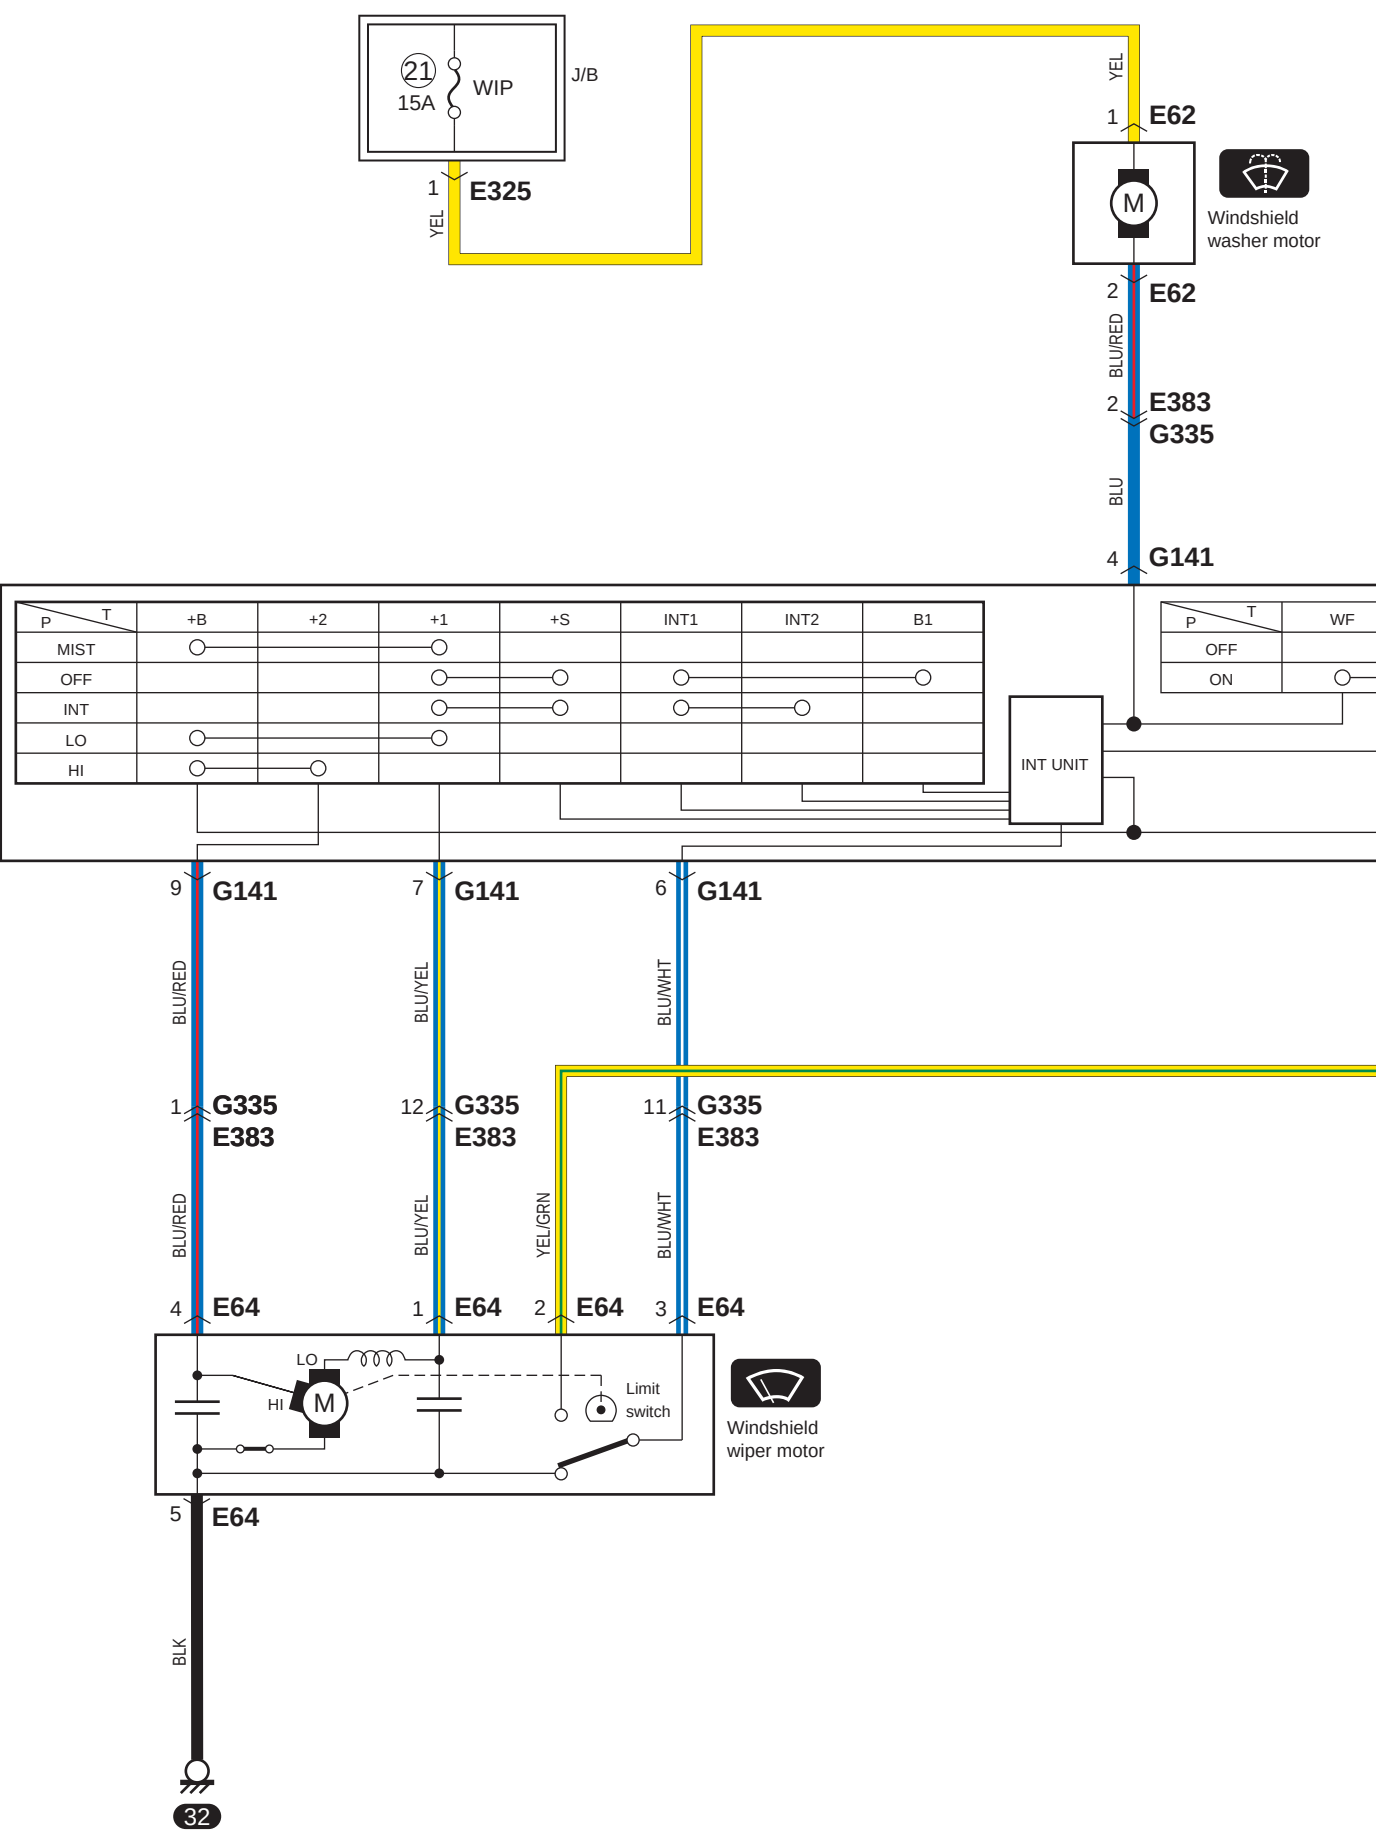

B-1 Ablaktörlő és ablakmosó kapcsolási rajza

