


B-4 Elektromos ablakok kapcsolási rajza

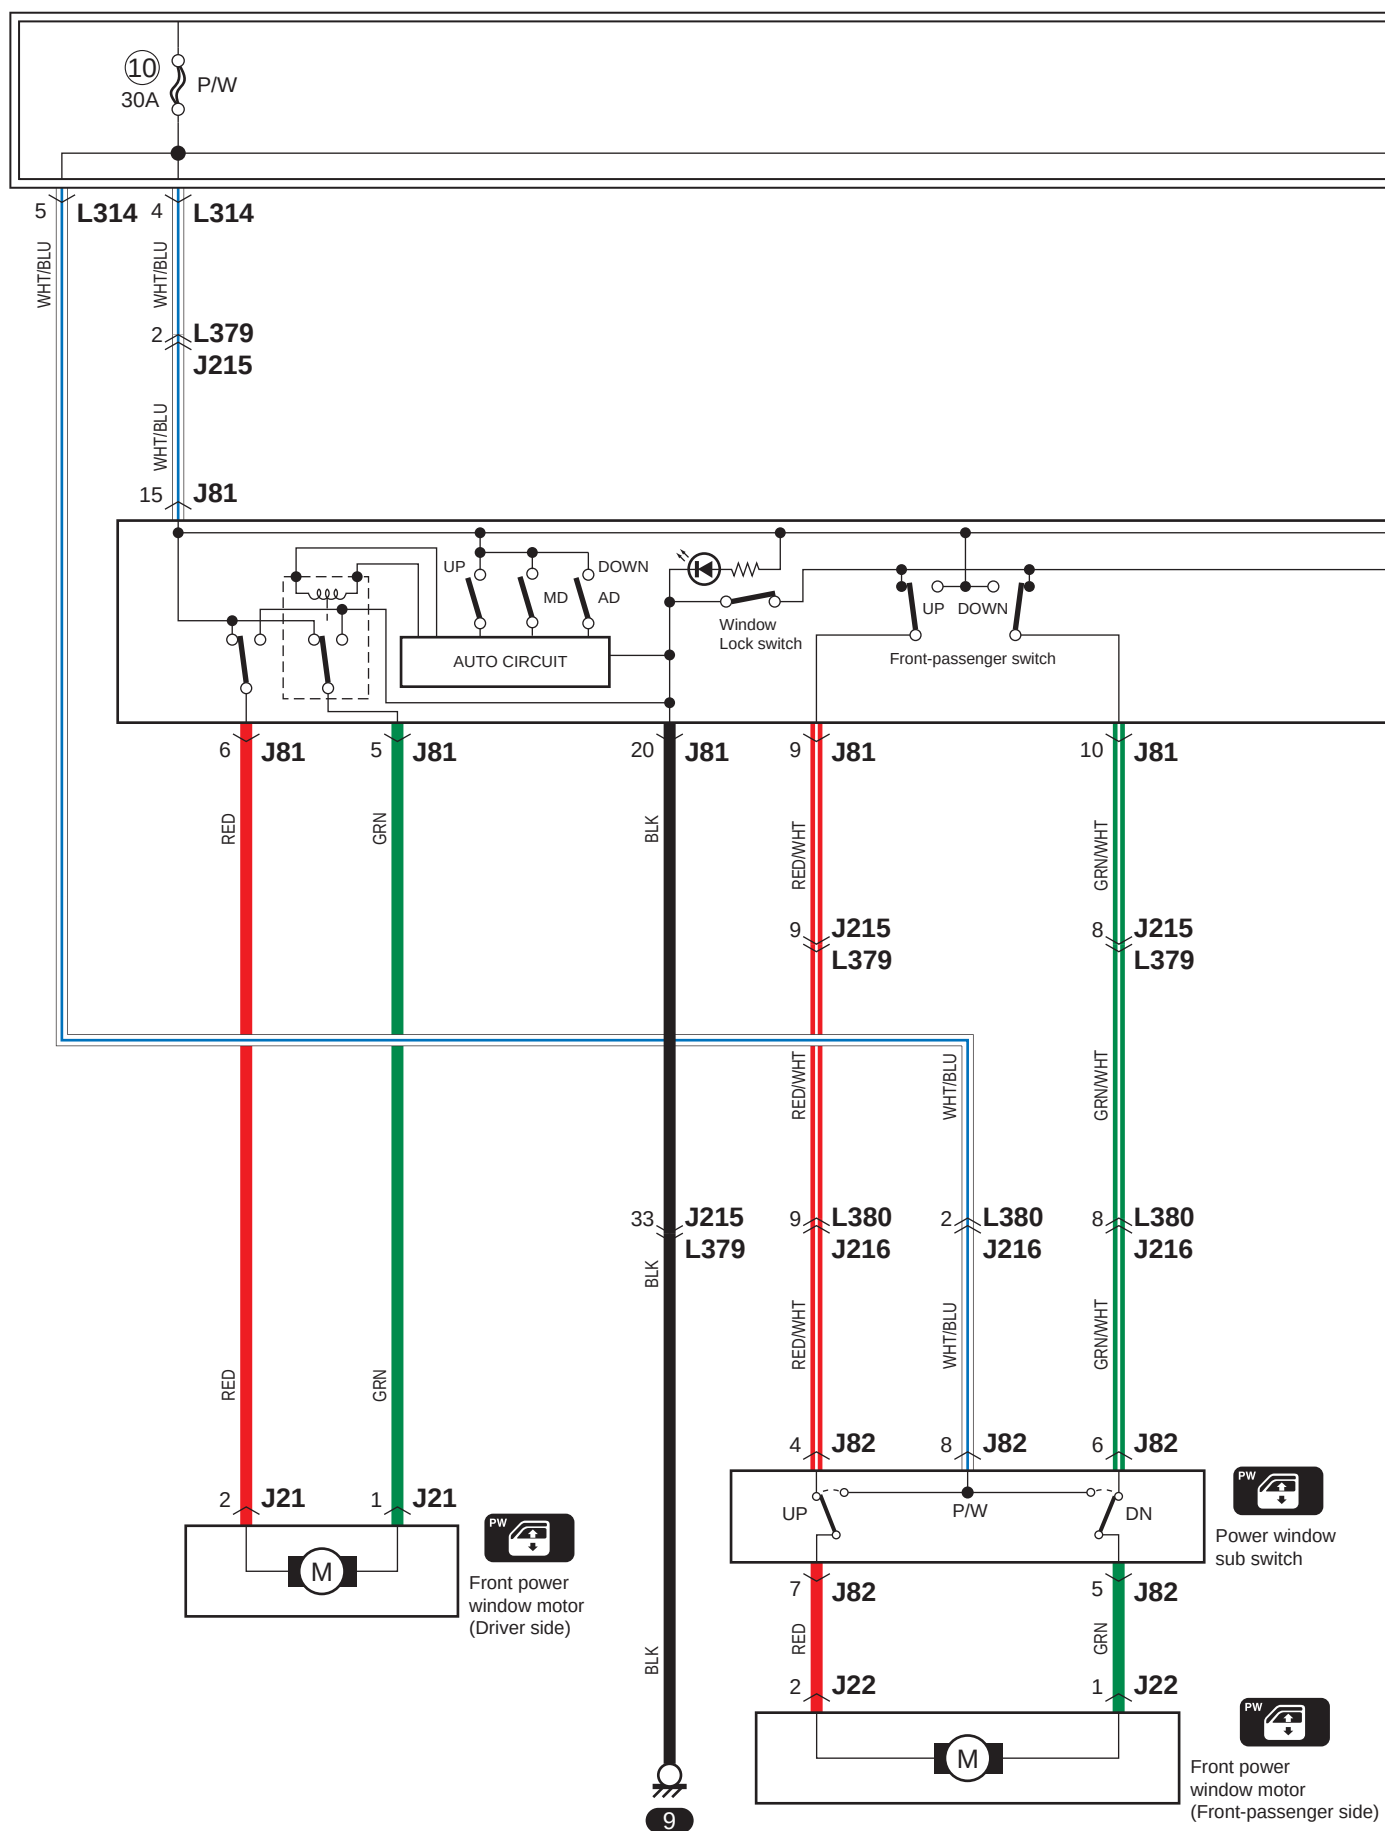

B-4 Elektromos ablakok kapcsolási rajza

