


B-4 Schema elettrico alzacristalli elettrici

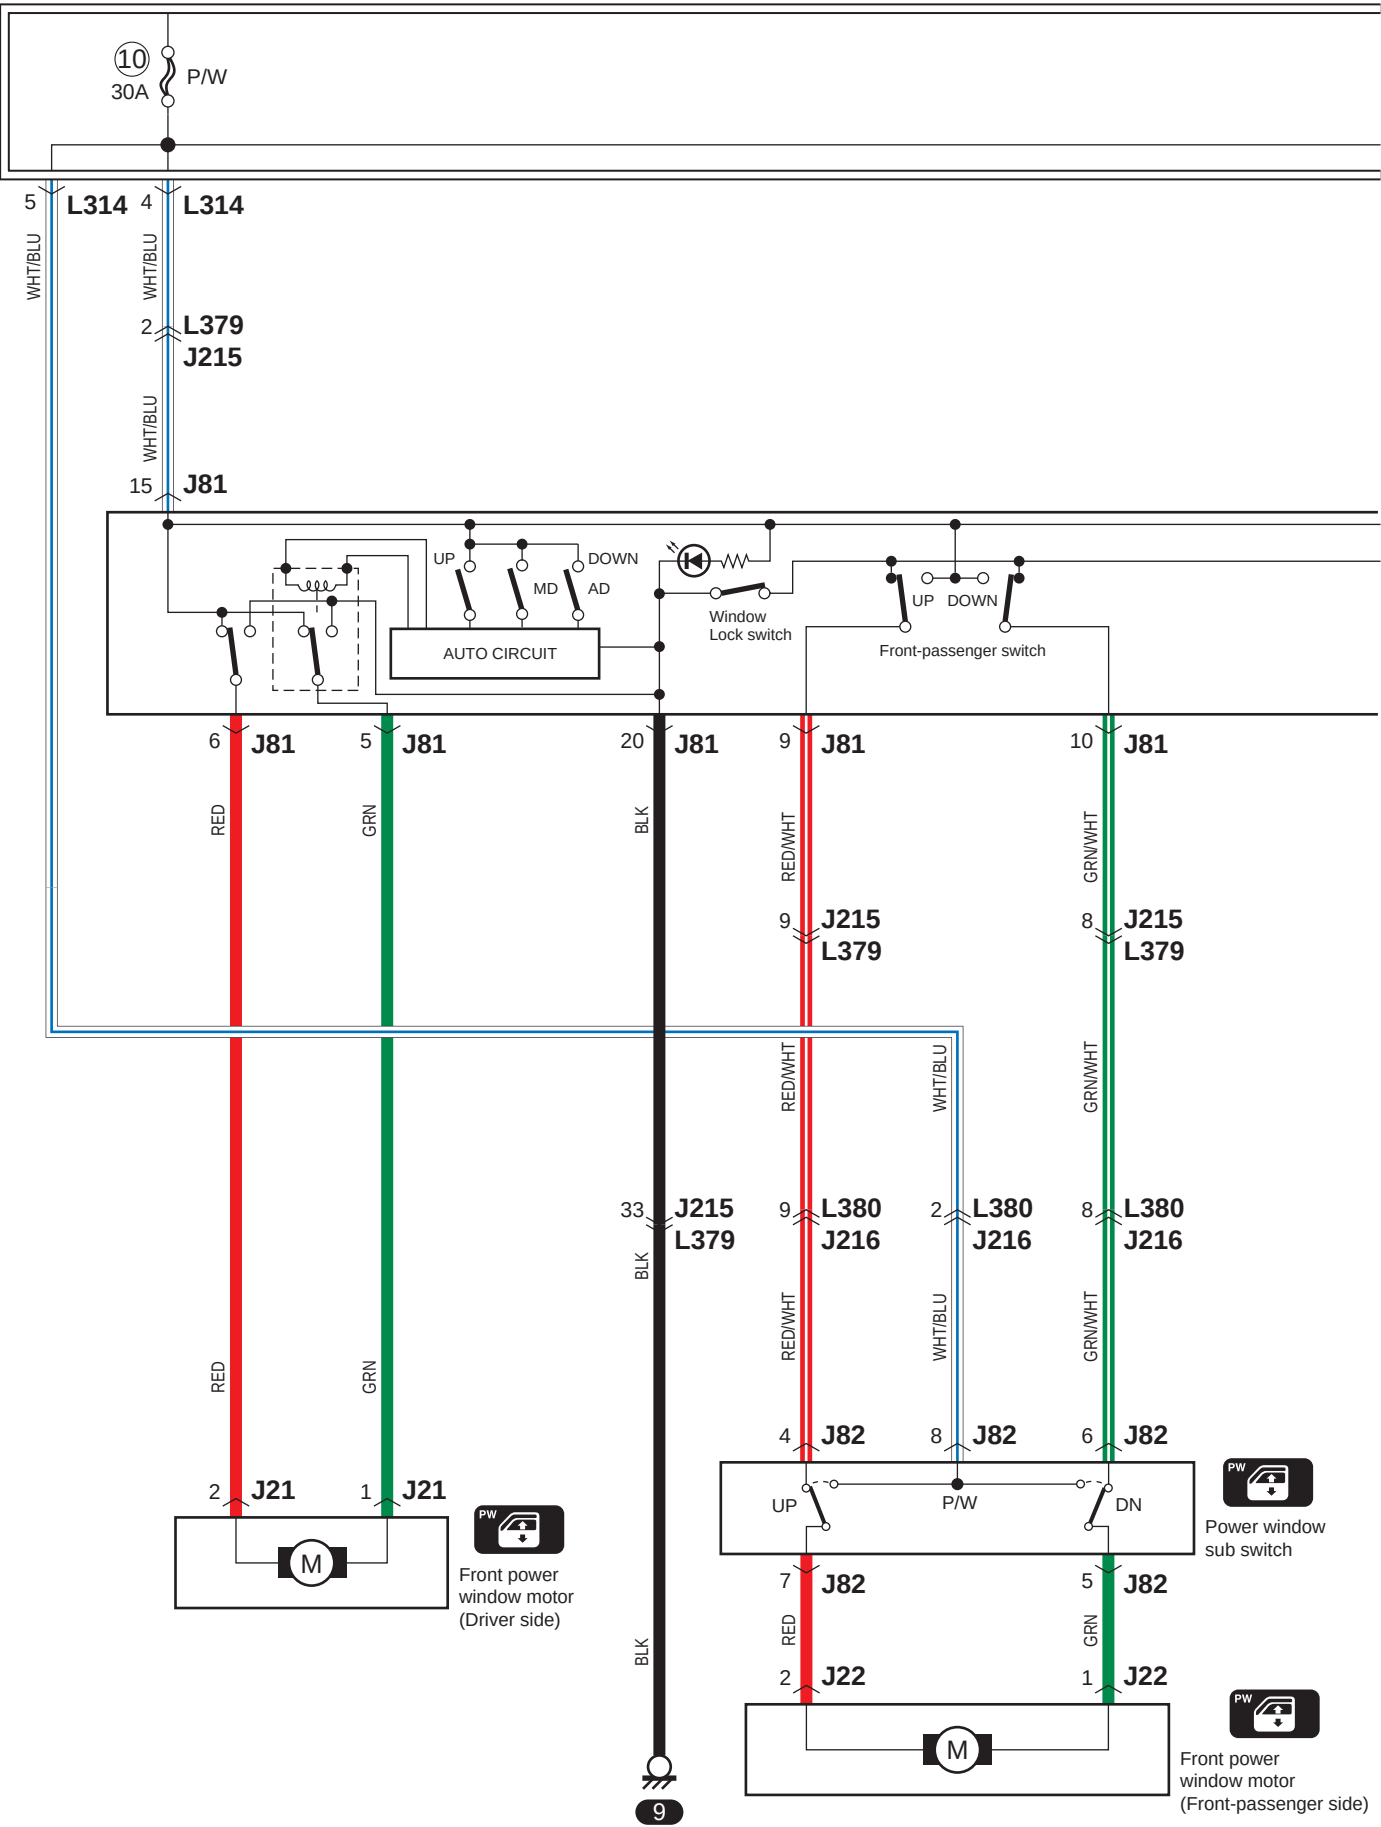

B-4 Schema elettrico alzacristalli elettrici

