




E-1-1 Schema elettrico dell'impianto A/C automatico

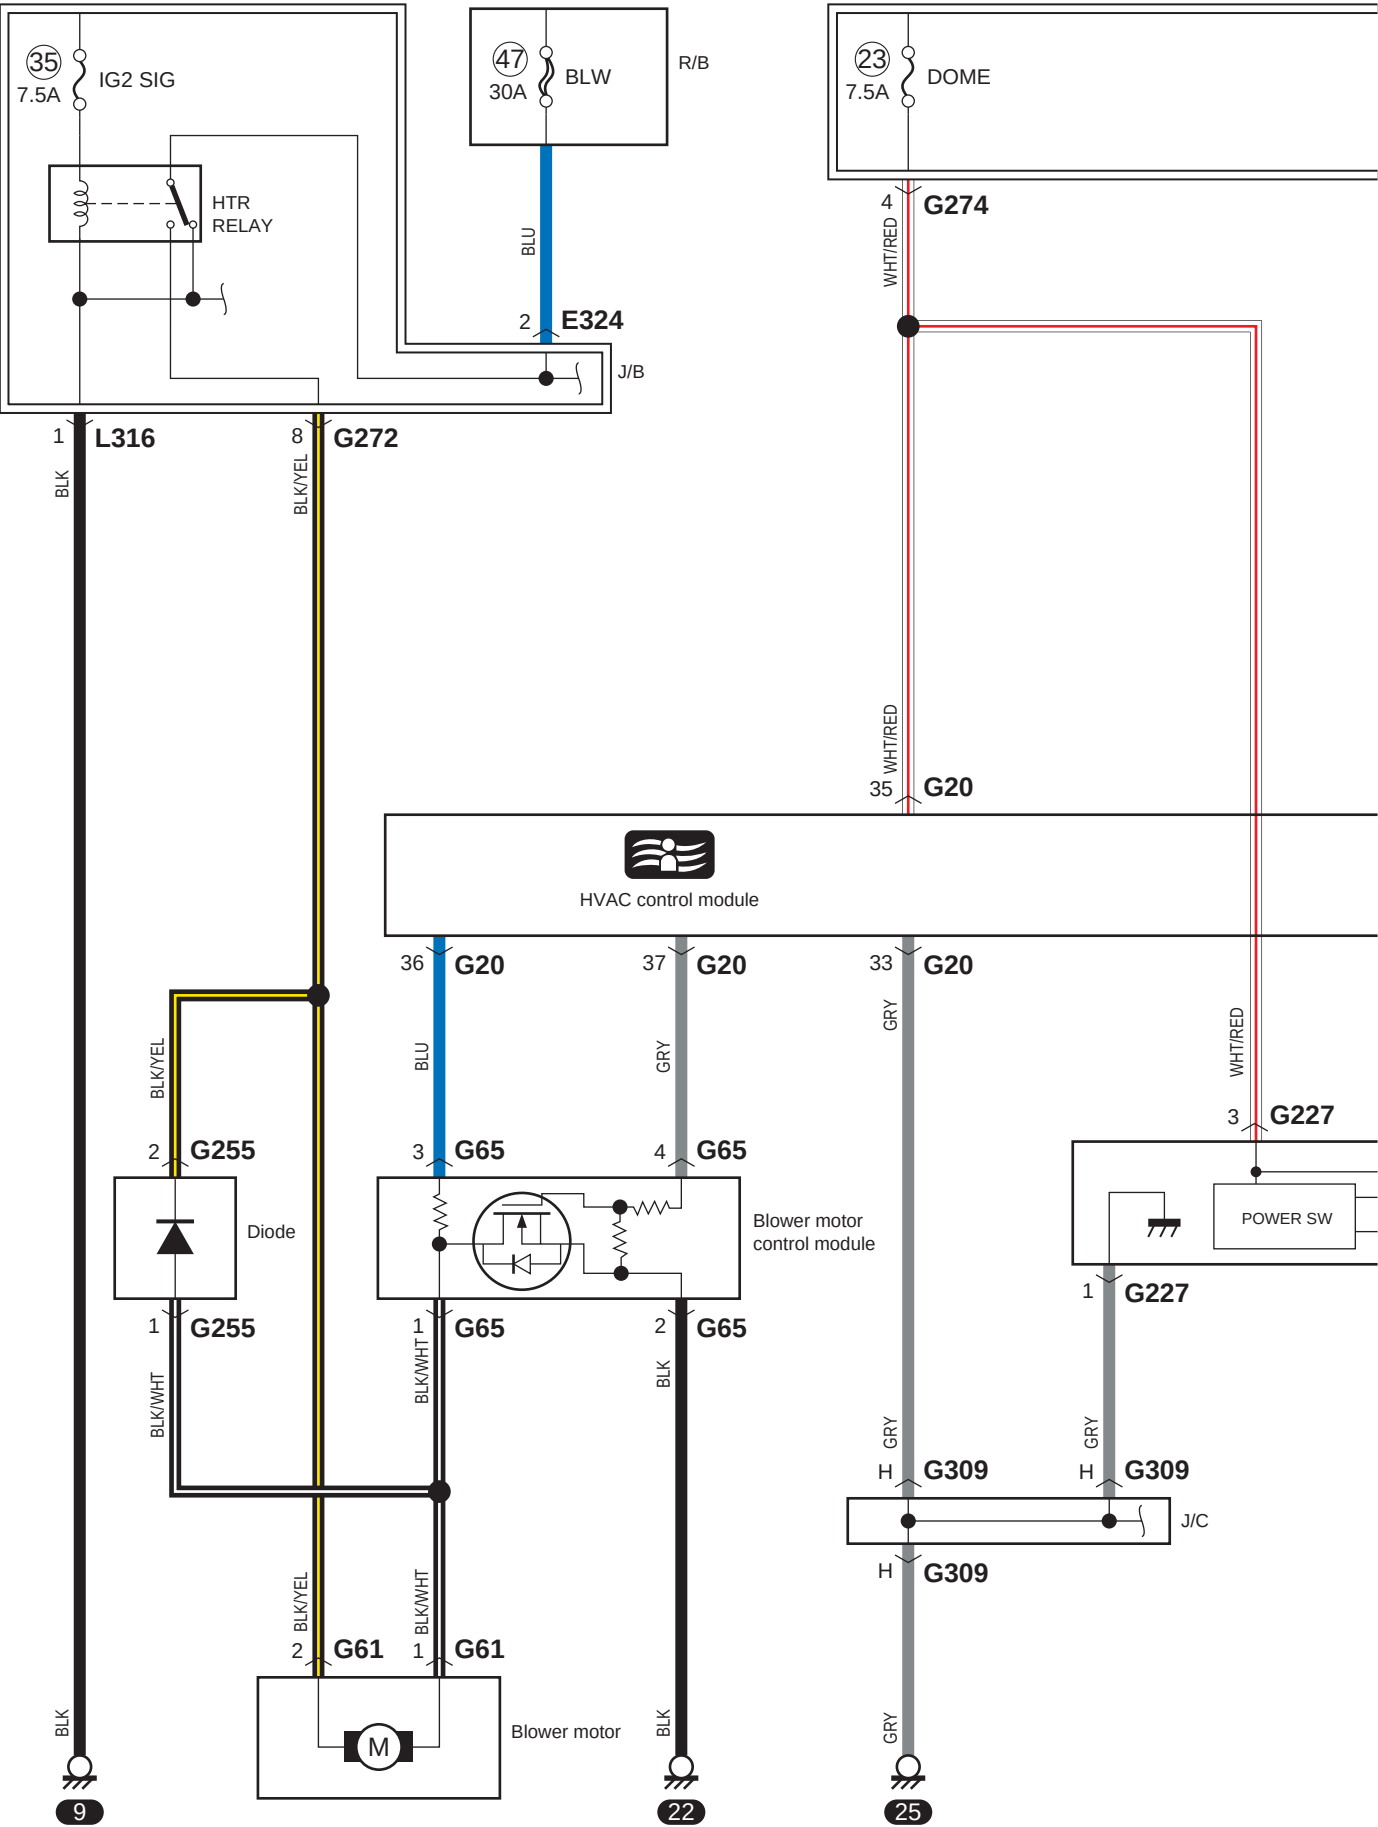

E-1-1 Schema elettrico dell'impianto A/C automatico

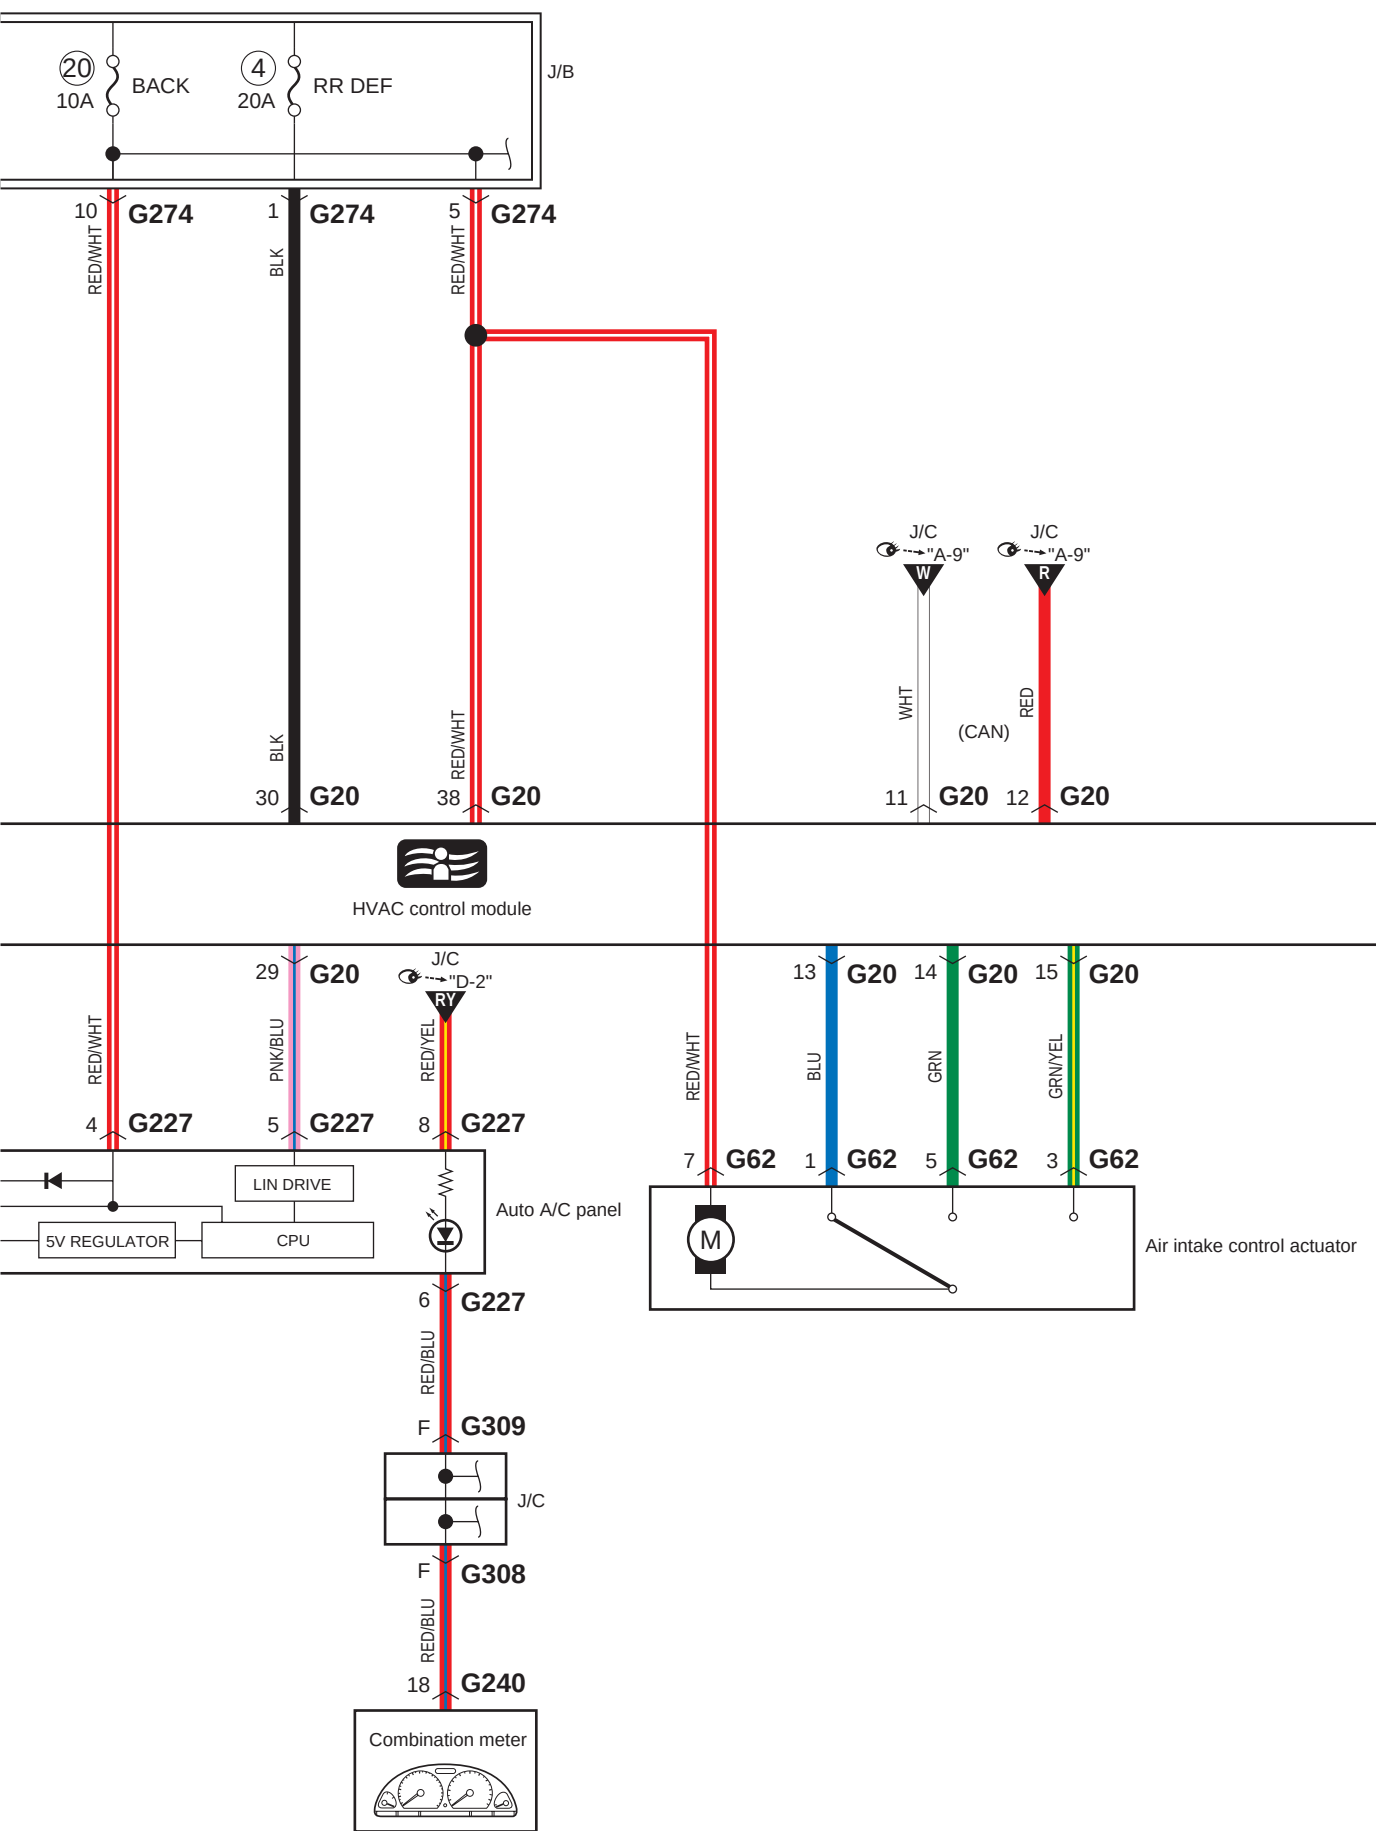

E-1-1 Schema elettrico dell'impianto A/C automatico

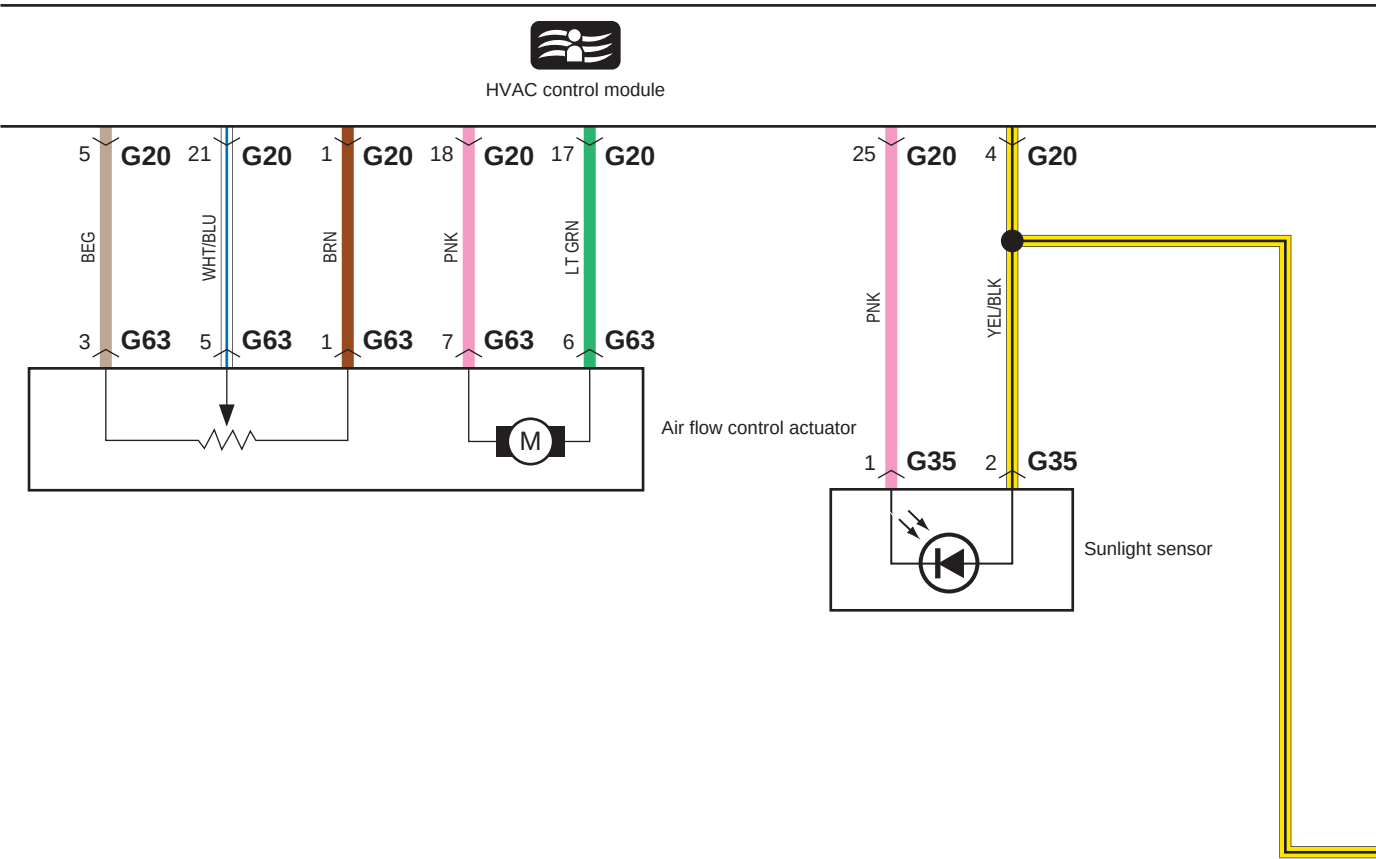

E-1-1 Schema elettrico dell'impianto A/C automatico

